


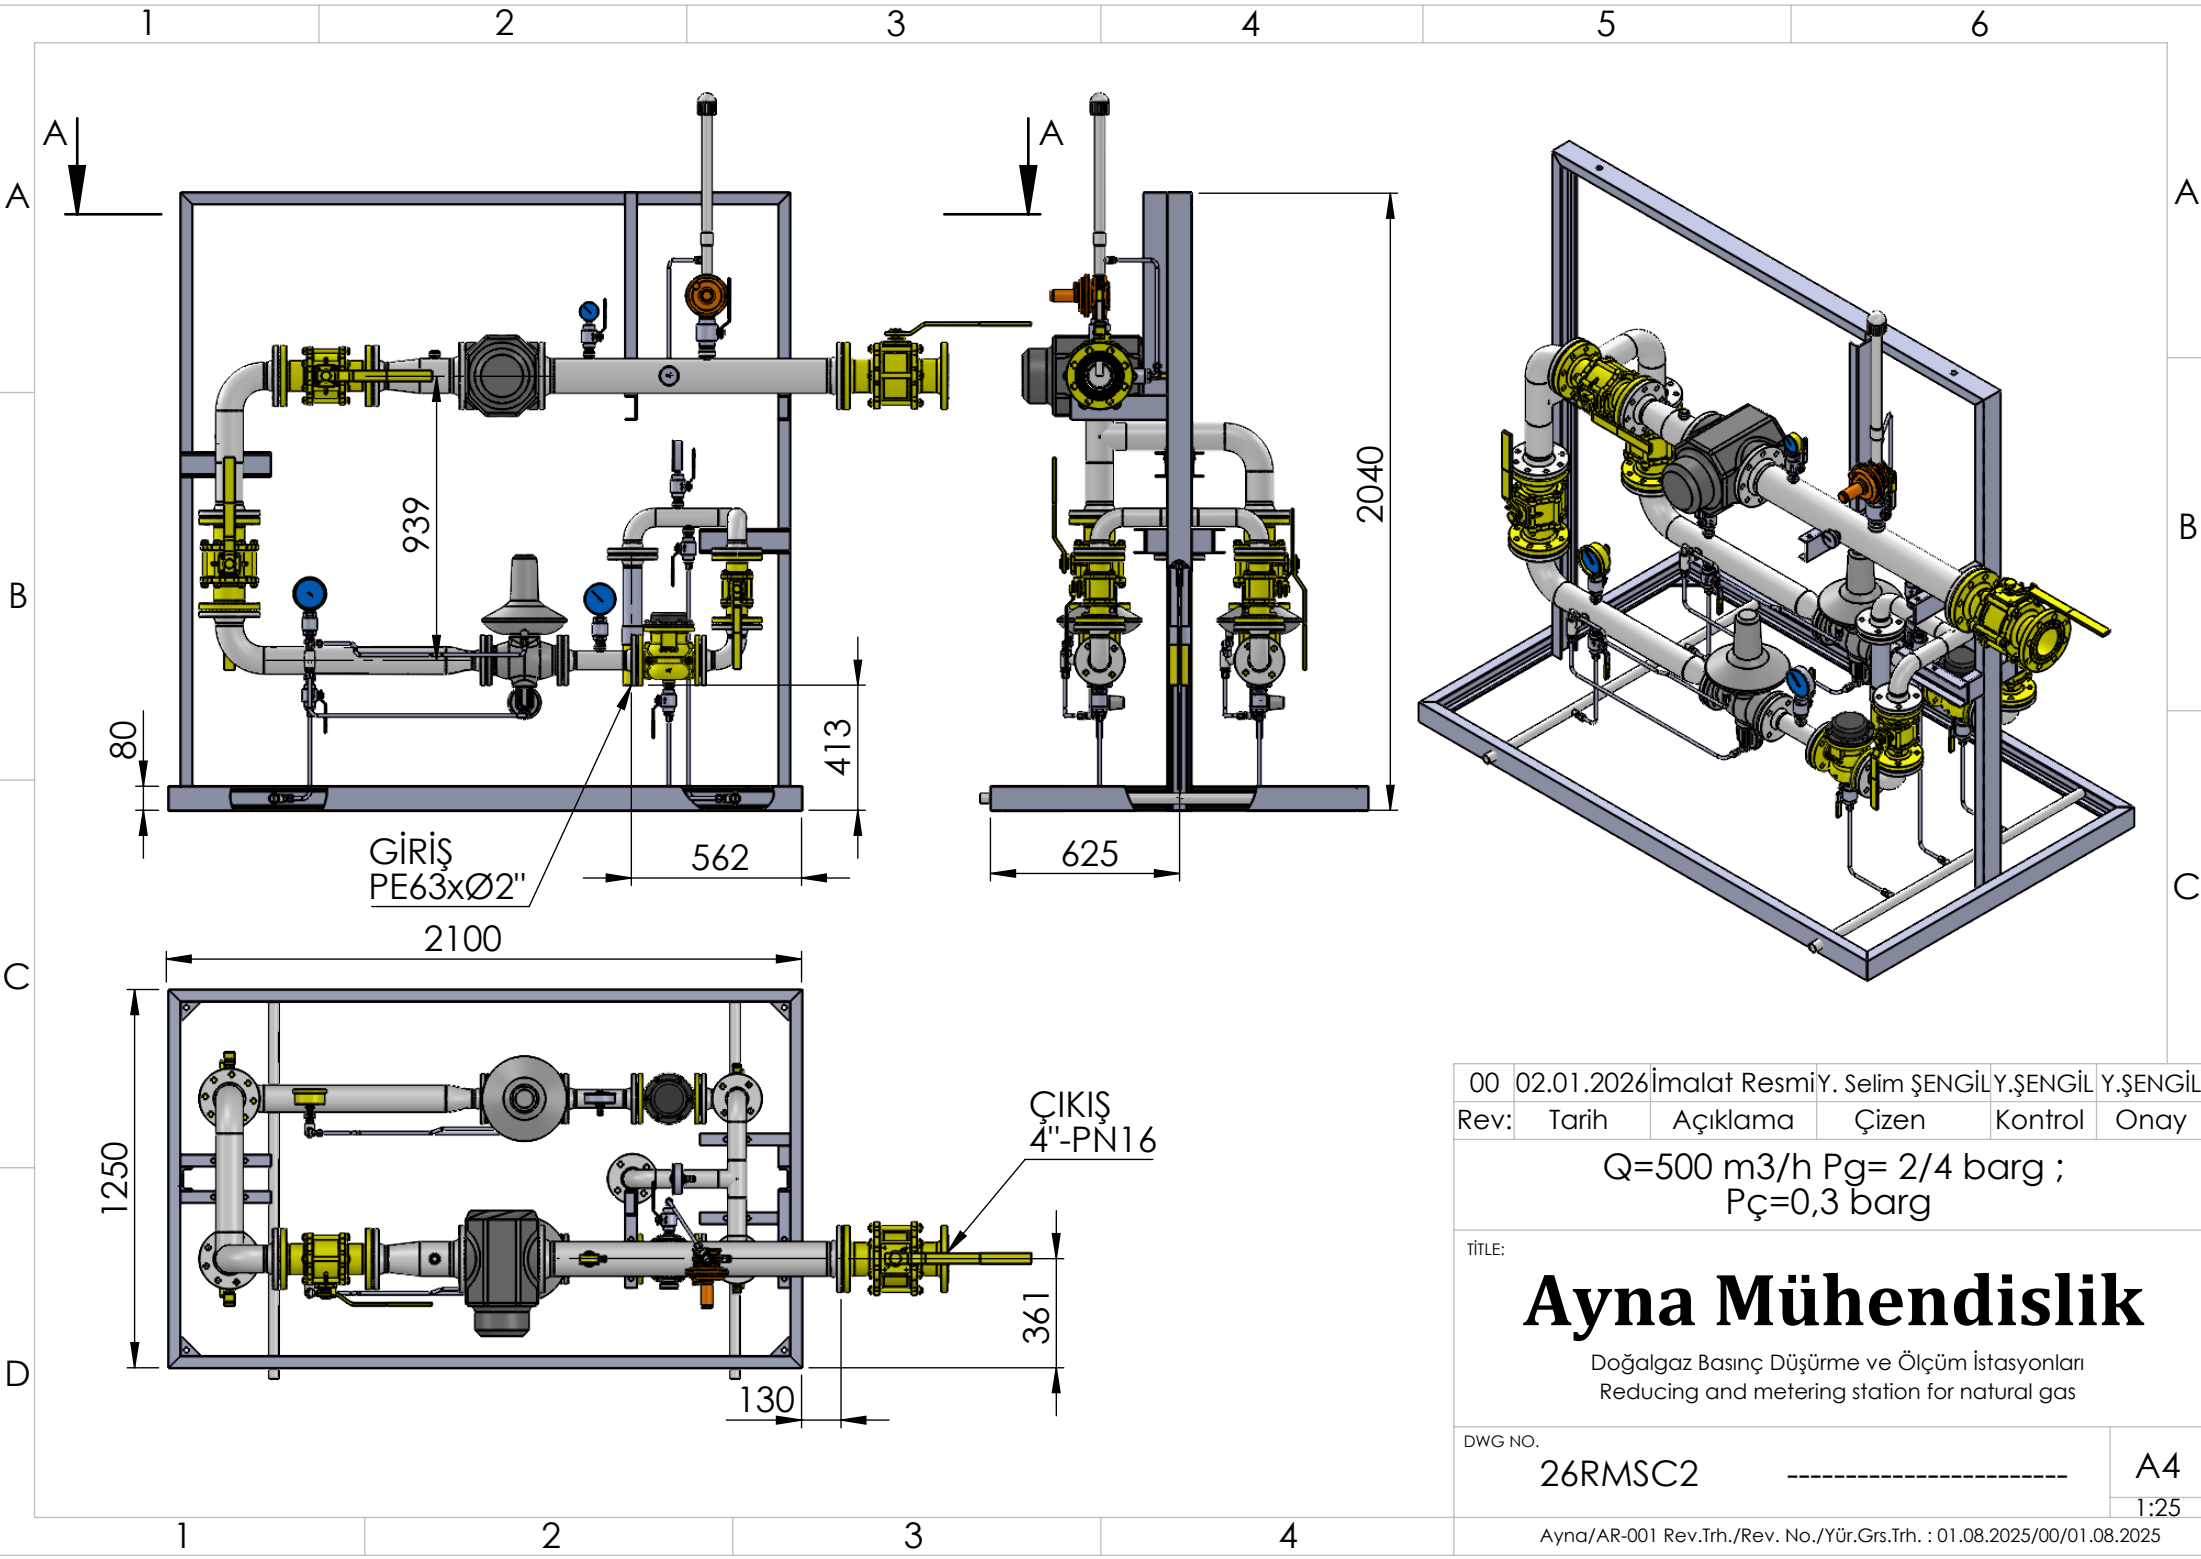

00	02.01.2026	İmalat Resmi	Y. Selim ŞENGİL	Y.ŞENGİL	Y.ŞENGİL
Rev:	Tarih	Açıklama	Çizen	Kontrol	Onay

Q=500 m³/h Pg= 2/4 barg ;
Pç=0,3 barg

TİTLE:

Ayna Mühendislik

Doğalgaz Basınç Düşürme ve Ölçüm İstasyonları
Reducing and metering station for natural gas

DWG NO.

26RMSC2

A4

1:25

Ayna/AR-001 Rev.Trh./Rev. No./Yür.Grs.Trh. : 01.08.2025/00/01.08.2025